



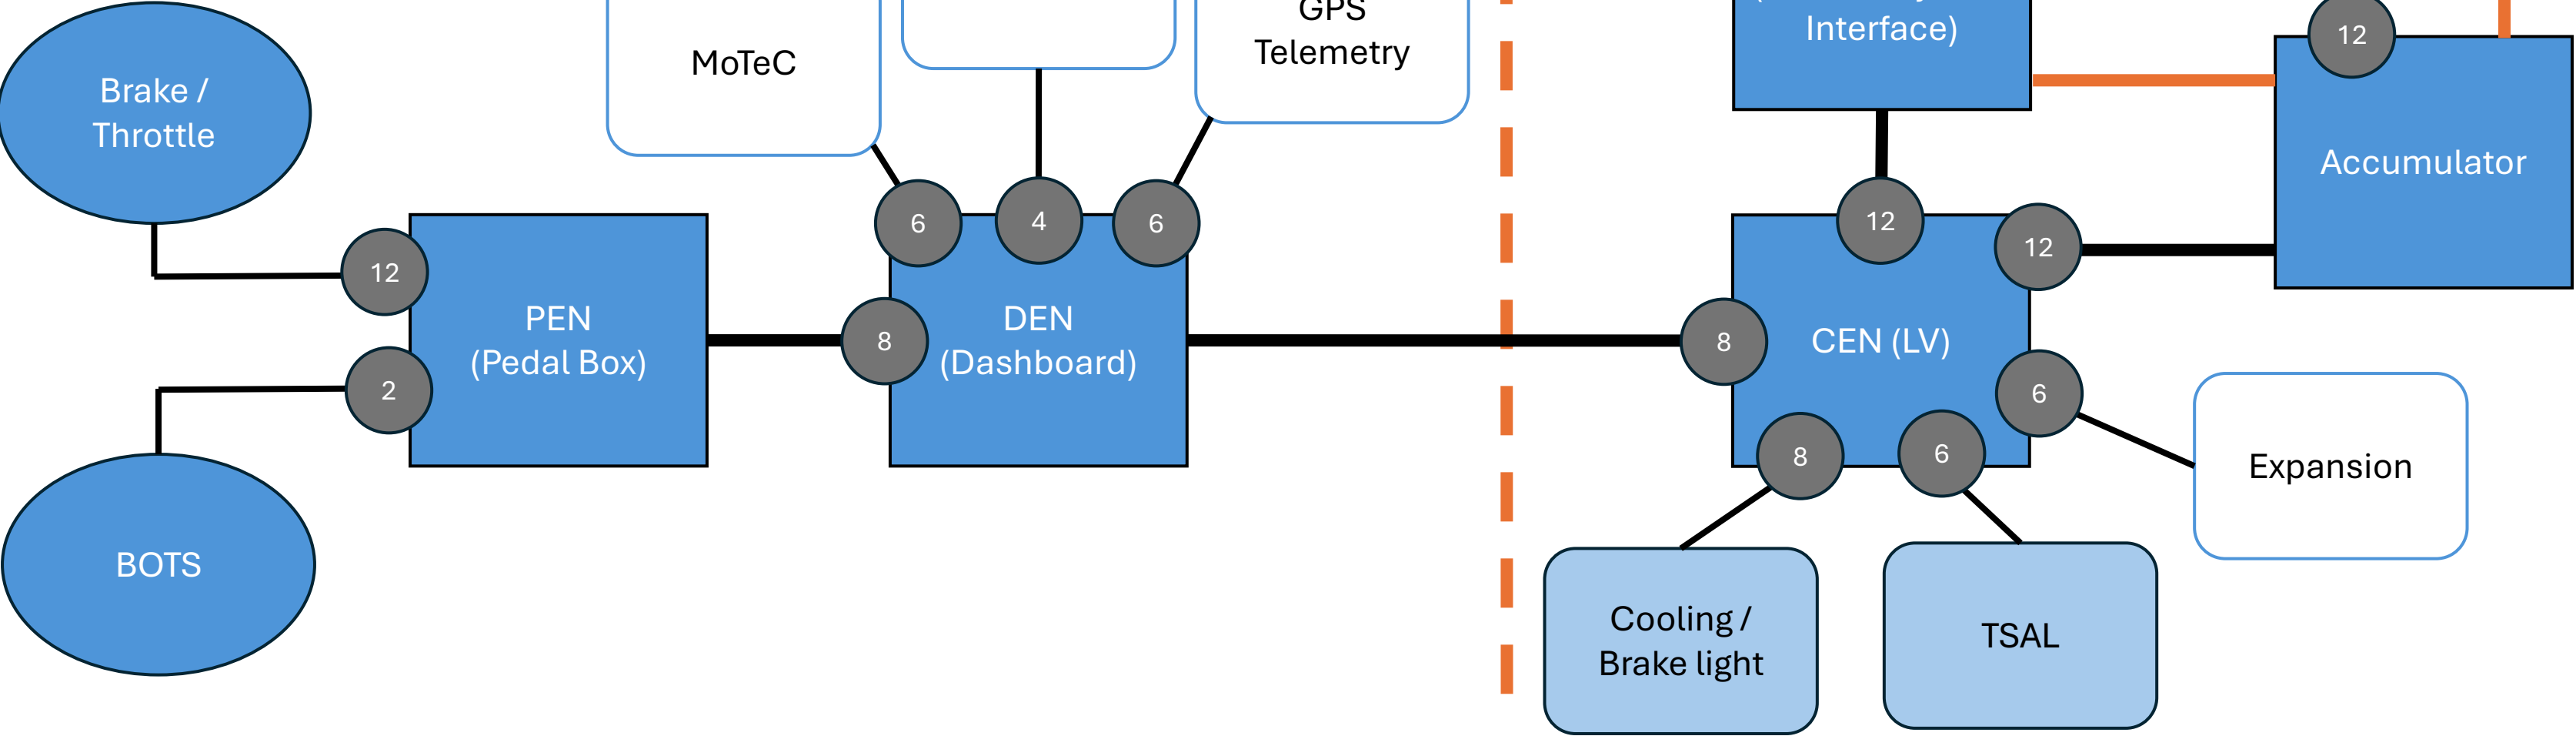


NU25 Electrical Topology



LEGEND

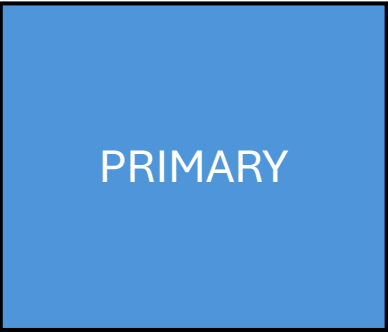


PRIMARY

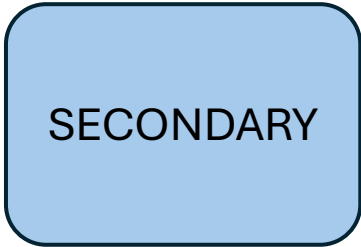

SECONDARY



OPTIONAL

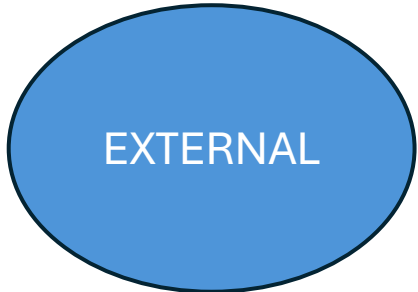

EXTERNAL



TRUNK



HIGH VOLTAGE



BRANCH